




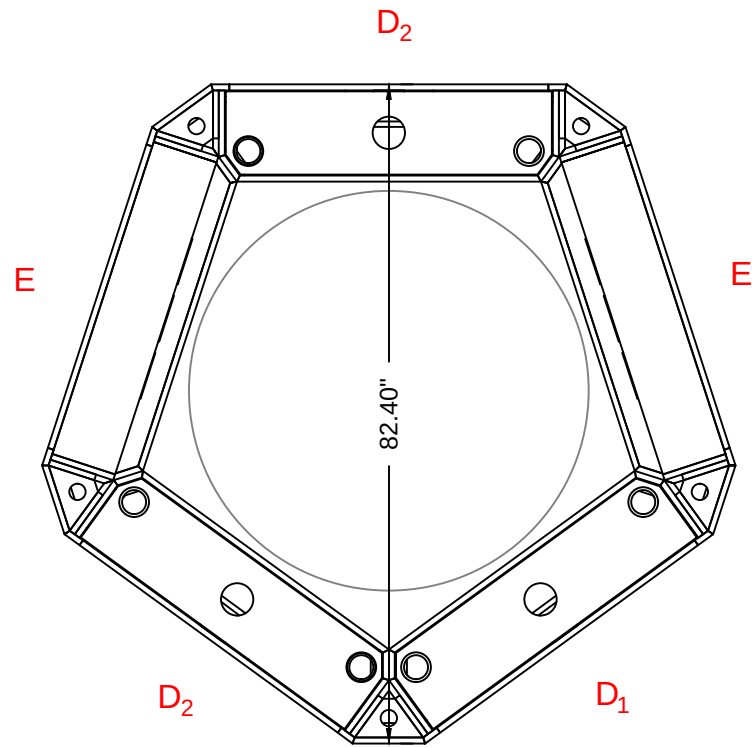


Column Plan View
SCALE: 1/2" = 1'-0"

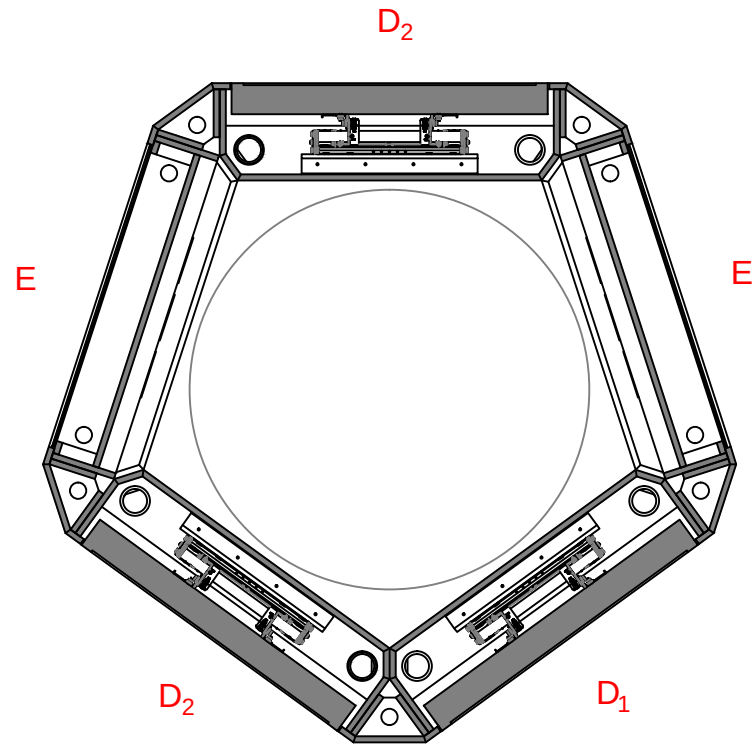


Column Section
SCALE: 1/2" = 1'-0"

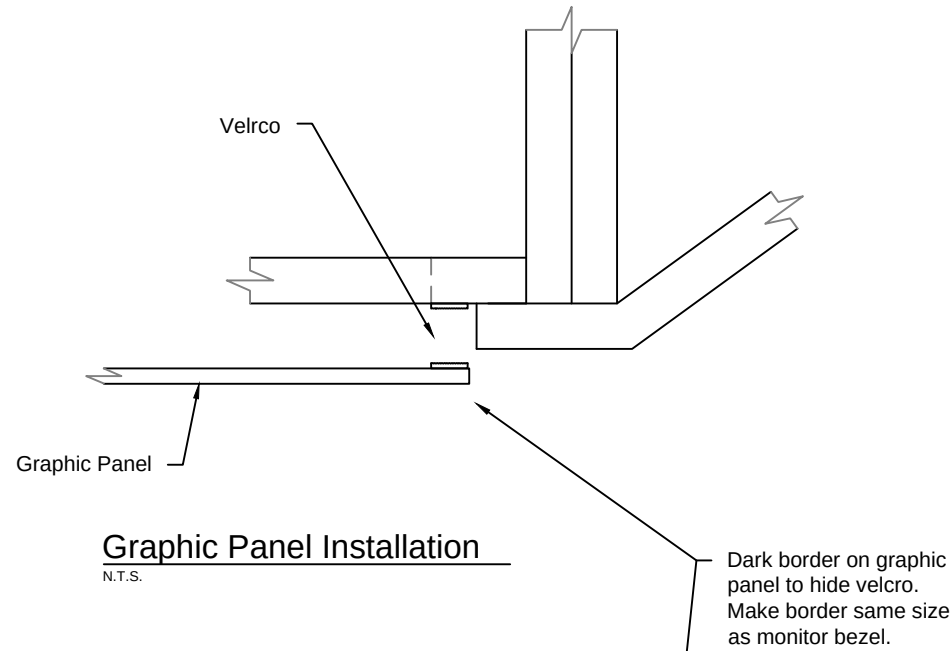

Graphic Panel Installation
N.T.S.

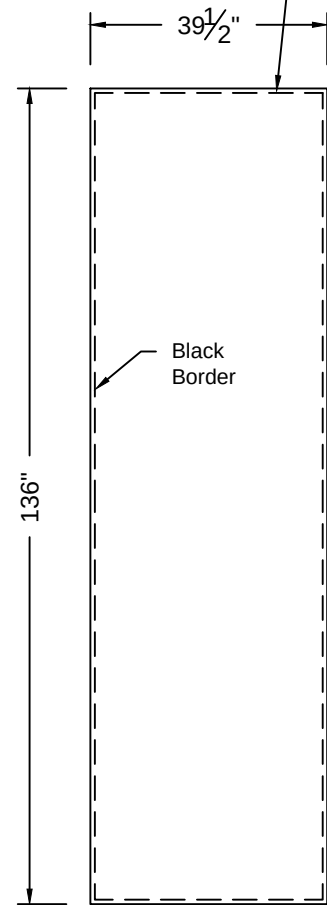


Back-Lit Graphic
Single Panel
SCALE: 3/8" = 1'-0"

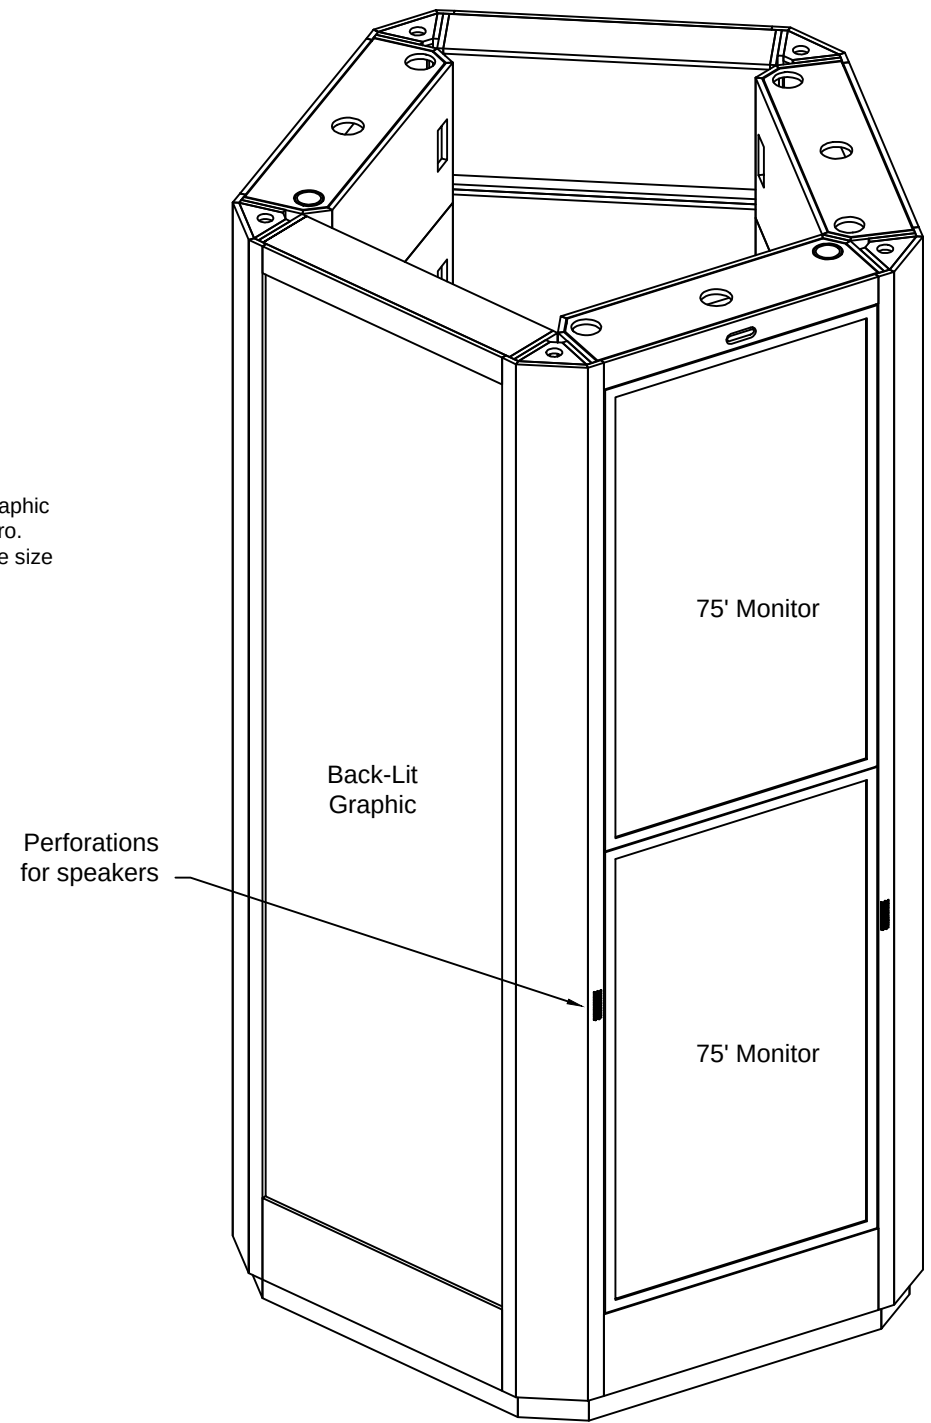


Perspective View
N.T.S.

 1301 GLENDALE MILFORD RD CINCINNATI, OHIO 45215 513.771.2339 FX 513.771.3521	CLIENT: Henry Ford Museum		SCALE:	REVISION: 11.16.18	DATE: 11.1.2018
	PROJECT MANAGER: Mike Murphy		ENGINEER: AHaycox	REVISION:	ENGINEER:
	SHOW DATE:		REVISION:	REVISION:	SHEET #: C-2
	BOOTH #:		REVISION:	REVISION:	JOB #: 127505
	SHEET NAME: Column Surround AV05		SHOW LOCATION: Detroit, MI	REVISION:	


SHEET SIZE IS 11x17

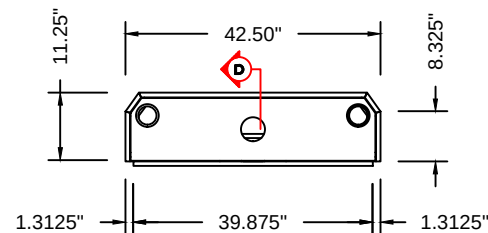

Plan View
SCALE: 3/8" = 1'-0"

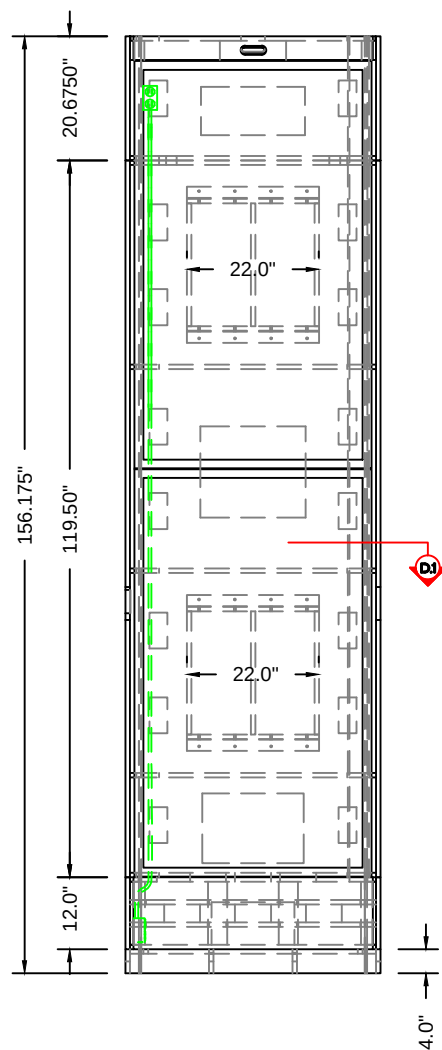

Front Elevation
SCALE: 3/8" = 1'-0"

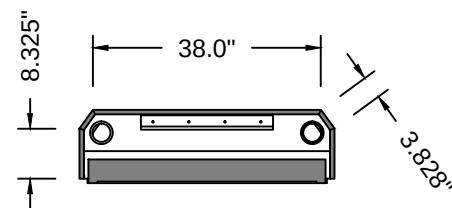


Section D.1
SCALE: 3/8" = 1'-0"




Type D Panel
D₁ - build qty (1)
D₂ - build qty (2)

D₁ & D₂ have identical construction but D₂ has (2) additions.

Addition 1: PVC wire chase
Addition 2: Add (2) electrical duplexes and conduit. See AV02 Type A panel for reference.

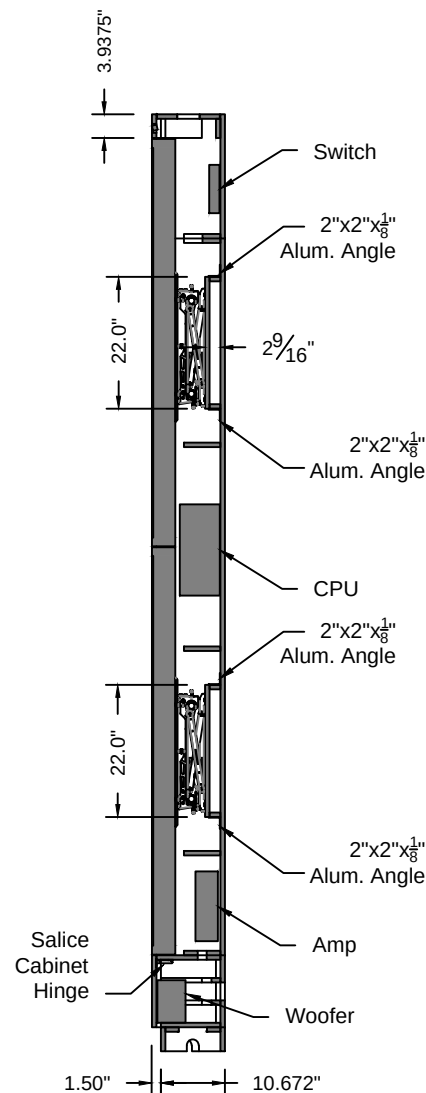


Section D
SCALE: 3/8" = 1'-0"

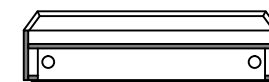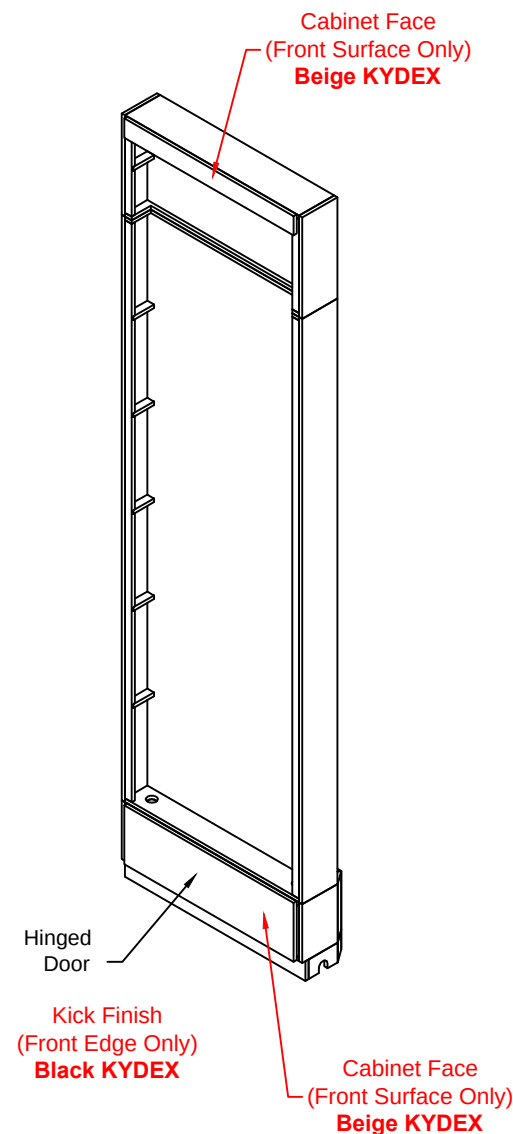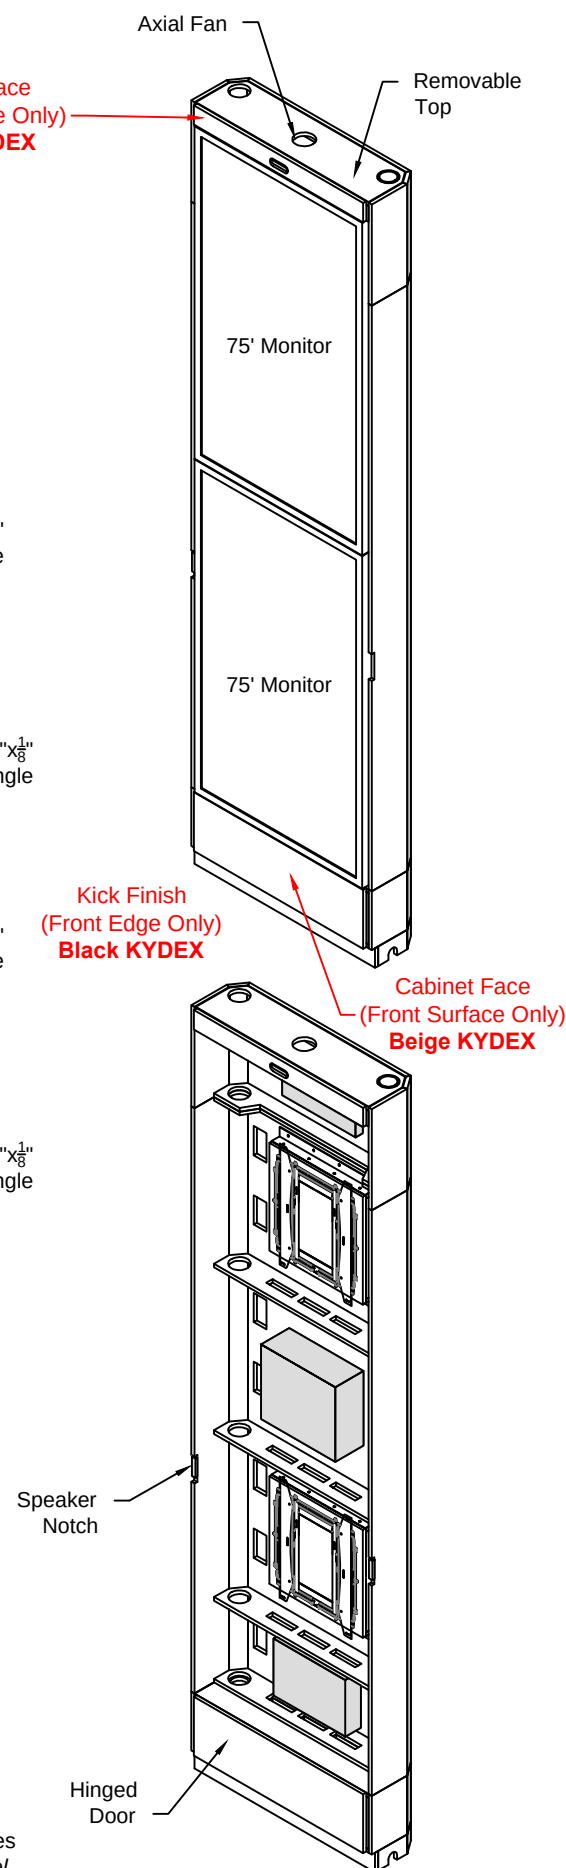


Section E.1
SCALE: 3/8" = 1'-0"


Type E Panel
Build Qty (2)

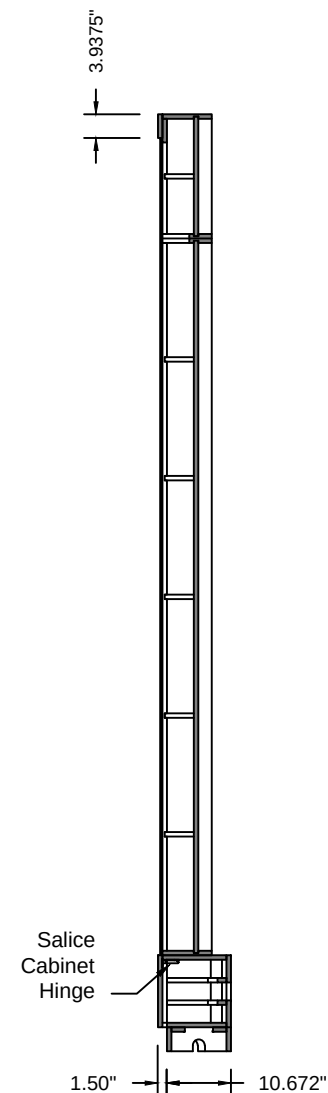

Section E
SCALE: 3/8" = 1'-0"

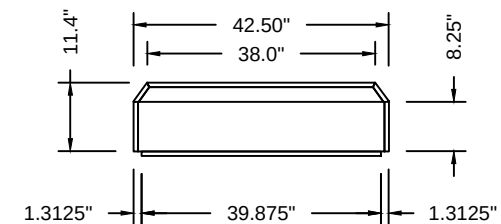


Plan View
SCALE: 3/8" = 1'-0"

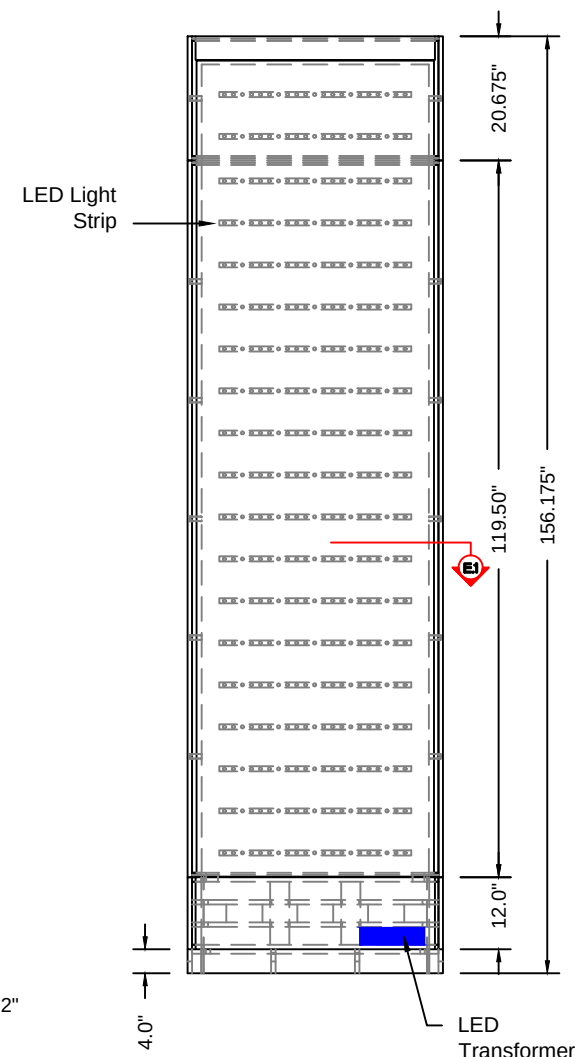


Front Elevation
SCALE: 3/8" = 1'-0"

 AD-EX INTERNATIONAL 1301 GLENDALE MILFORD RD CINCINNATI, OHIO 45215 513.771.2339 FX 513.771.3521	CLIENT:	Henry Ford Museum	SCALE:	REVISION: 11.16.18	© DATE : 11.1.2018
			PROJECT MANAGER: Mike Murphy	REVISION:	ENGINEER: AHaycox
			SHOW DATE:	REVISION:	SHEET #: C-2.1
			BOOTH #:	REVISION:	JOB #:
			SHOW NAME:	REVISION:	127505
			SHOW LOCATION: Detroit, MI	REVISION:	
	BOOTH SIZE:				
	SHEET NAME:	Column Surround AV05			

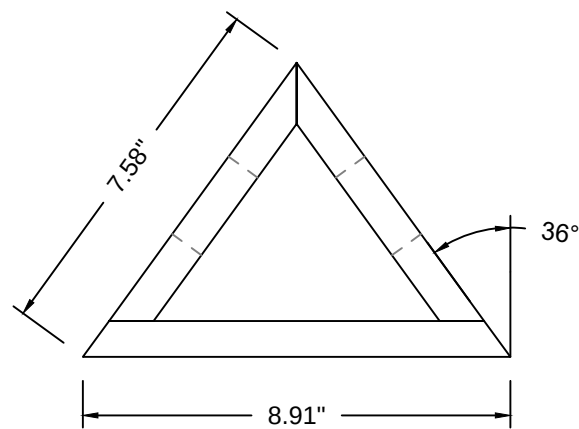


Plan View
SCALE: 1-1/2" = 1'-0"


Kick Filler
Build Qty (5)

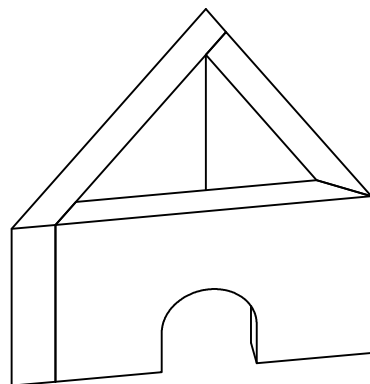


Perspective
N.T.S.

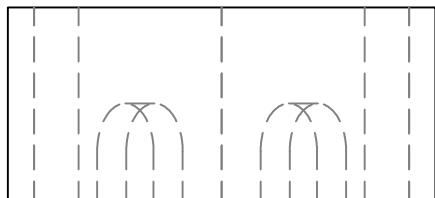


Front Elevation
SCALE: 1-1/2" = 1'-0"

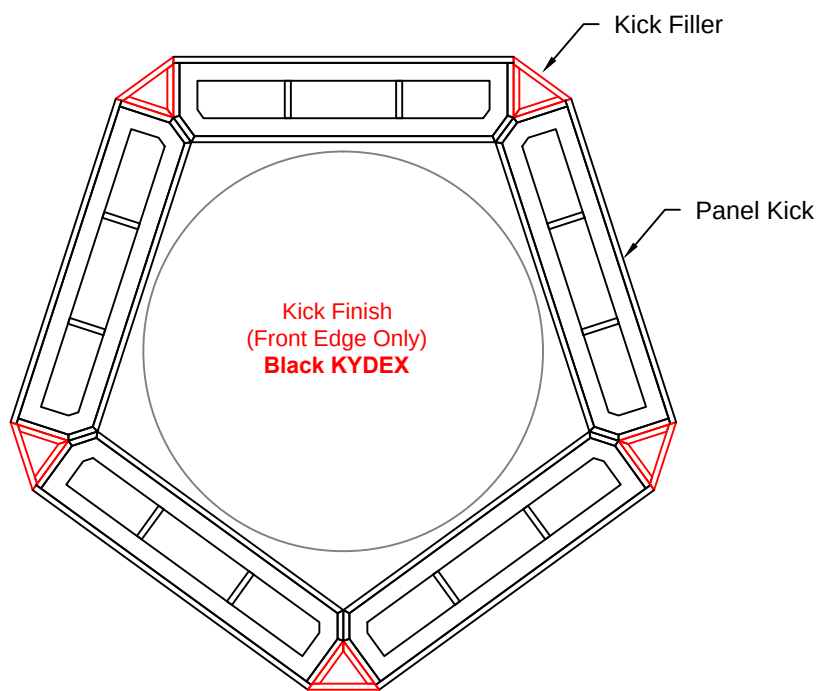

Typical Column Surround
SCALE: 1/2" = 1'-0"

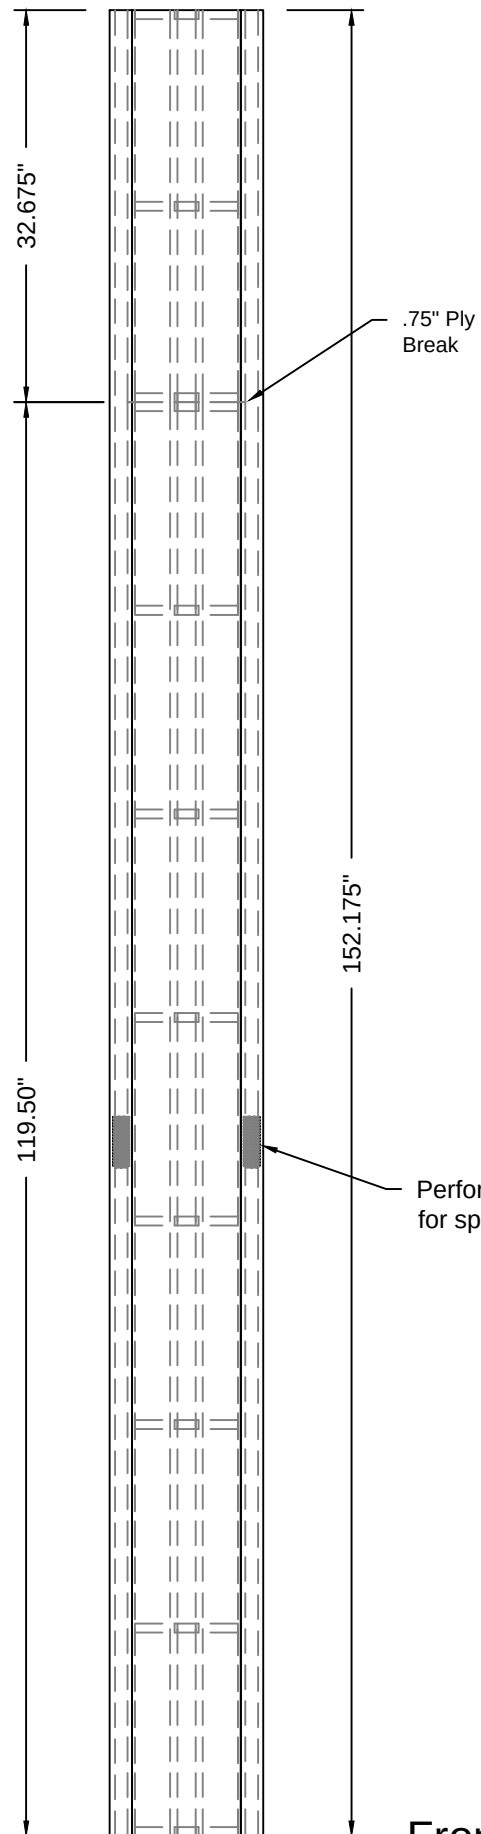


Front Elevation
SCALE: 3/4" = 1'-0"

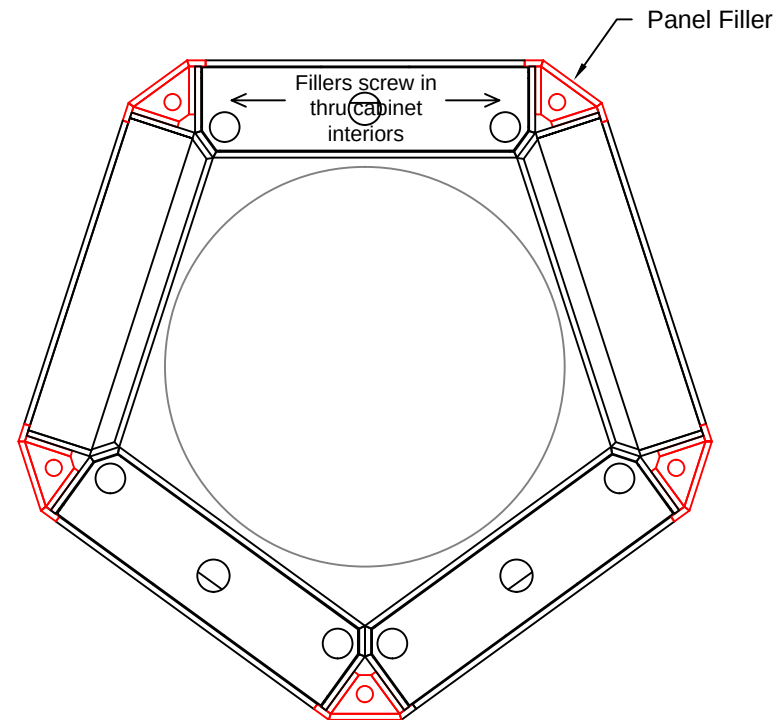


Typical Column Surround
SCALE: 1/2" = 1'-0"

Note: Exterior face = .75" MDF
Interior ribbing = .75" Plywood

Cabinet Filler
Build Qty (5)

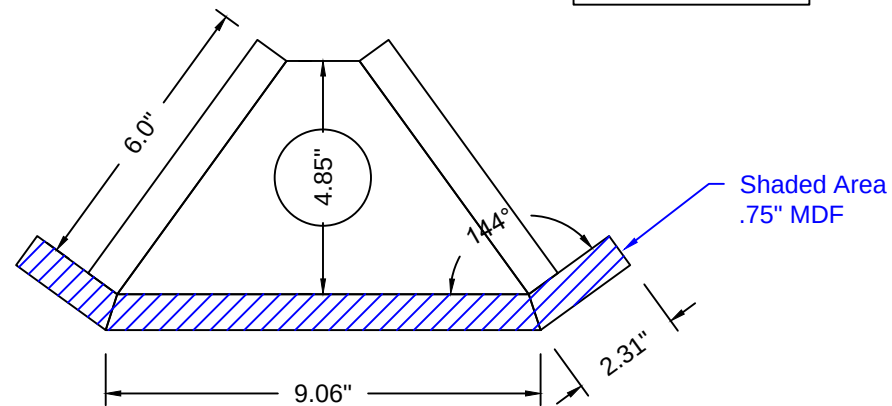

Plan View
SCALE: 3" = 1'-0"

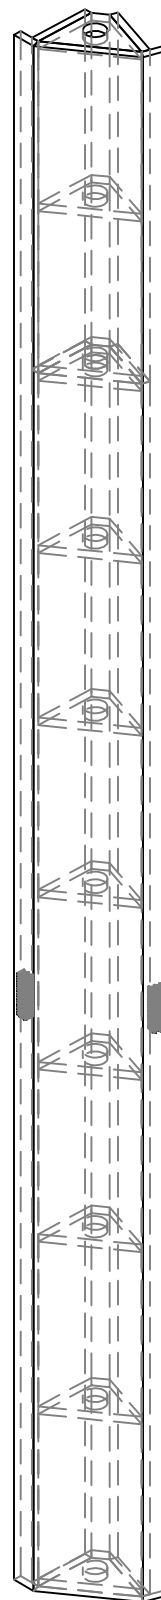

 1301 GLENDALE MILFORD RD CINCINNATI, OHIO 45215 513.771.2339 FX 513.771.3521	CLIENT: Henry Ford Museum BOOTH SIZE: SHEET NAME: Column Surround AV05	SCALE:	REVISION: 11.16.18	© DATE : 11.1.2018
		PROJECT MANAGER: Mike Murphy	REVISION:	ENGINEER: AHaycox
		SHOW DATE:	REVISION:	SHEET #: C-2.2
		BOOTH #:	REVISION:	JOB #:
		SHOW NAME:	REVISION:	127505
		SHOW LOCATION: Detroit, MI	REVISION:	